PROVINCIA DE SAN LUIS	4	237	21

Departamento: CHACABUCO

Partido: LARCA

Lugar: Ruta Provincial Nº1-Km 27-Villa Larca

Objeto: MENSURA, UNIFICACION y DIVISION

Propietarios

LOS CERRITOS S.R.L.

(CUIT: 33-71136771-9)

INSCRIPCION DE DOMINIO	PADRON	RECEPTORIA
Matricula Nº6-4825- R:6- A2	967691,967692,967693, 967694,967695,967696, 967697,967698,967699, 967700,967701,967702, 967703,967704,967705, 967706,967707,967708, 967709,967710,967711, 967712,967713,967714, 967715,967716,967717, 967718,967719,967720, 967721,967722,967723, 967724, 967725,967726.	Concaran

NOMENCLATURA CATASTRAL DE ORIGEN

Circunscripción	Cuadrante	Seccion	Manzana	Parcela
Villa Larca	----------	----------	210	1 a 36

NOTA OFICIAL: Se encuentra afectado por Ley Nº IX-0332-2004 (5538"R")343Creaciòn "Parque Provincial Presidente Peròn" y Area Natural Protegida de la Provincia de San Luis, Decreto Nº3220-MMA-2011 y Resoluciòn Nº1 PGA y PGB-2014. Area "B" Reservada.

NOTA OFICIAL:"El presente plano ha sido rubricado con firma digital-Ley Provincial NºV-0591-2007".

OBSERVACIONES: Los vértices fueron materializados con estacas y postes de madera.
La presente unifica las parcelas Nº1 a 36 de la manzana Nº210 del Pl.Nº4/33/13, confeccionado por el suscripto y visado con fecha 11 de Septiembre de 2013 y luego la divide.
Los lados de las parcelas que no tienen el tipo de cierre indicado son sin cierre existente.
Autorizado por Decreto Nº64-M.M.A.-2011.
Las diferencias existentes en el presente plano con respecto al antedente en cuanto a las medidas lineales y ángulares han sido modificadas al solo efecto de producir en cierre del poligono origen.

San Luis 10 de Marzo de 2018

Ing.Agrim. Mario Ruiz - Mat.N° 247 C.A.S.L.

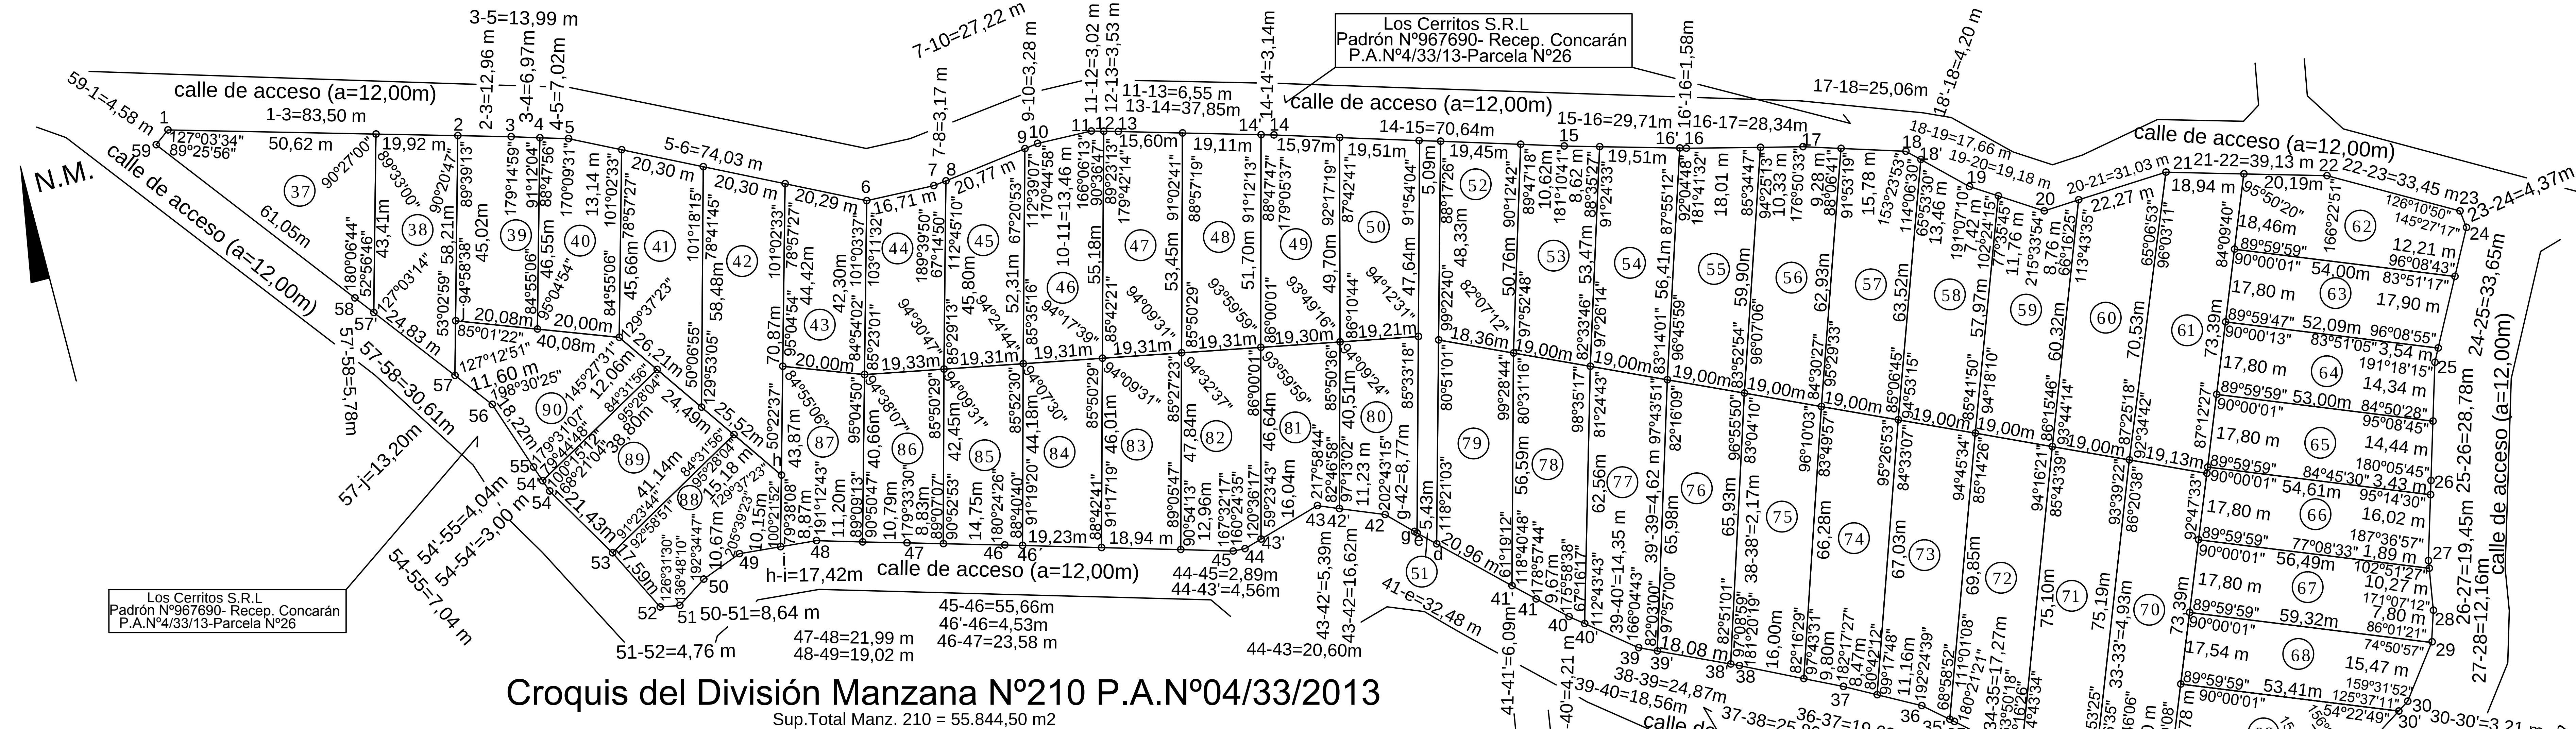

Croquis del División Manzana Nº210 P.A.Nº04/33/2013

Sup.Total Manz. 210 = 55.844,50 m2

RESUMEN DE SUPERFICIES

MANZANA 210	Padrón	Recep.	Secc.	Edif.
PARCELA N°37 = 1.251,30 m2	1074754	10	02	baldio
PARCELA N°38 = 1.010,00 m2	1074755	10	02	baldio
PARCELA N°39 = 914,60 m2	1074756	10	02	baldio
PARCELA N°40 = 926,30 m2	1074757	10	02	baldio
PARCELA N°41 = 1.042,90 m2	1074758	10	02	baldio
PARCELA N°42 = 1.278,40 m2	1074759	10	02	baldio
PARCELA N°43 = 863,60 m2	1074760	10	02	baldio
PARCELA N°44 = 842,70 m2	1074761	10	02	baldio
PARCELA N°45 = 942,10 m2	1074762	10	02	baldio
PARCELA N°46 = 1.042,00 m2	1074763	10	02	baldio
PARCELA N°47 = 1.042,40 m2	1074764	10	02	baldio
PARCELA N°48 = 1.008,80 m2	1074765	10	02	baldio
PARCELA N°49 = 972,90 m2	1074766	10	02	baldio
PARCELA N°50 = 940,90 m2	1074767	10	02	baldio
PARCELA N°51 = 476,40 m2	1074768	10	02	baldio
PARCELA N°52 = 931,10 m2	1074769	10	02	baldio
PARCELA N°53 = 990,90 m2	1074770	10	02	baldio
PARCELA N°54 = 1.053,60 m2	1074771	10	02	baldio
PARCELA N°55 = 1.116,70 m2	1074772	10	02	baldio
PARCELA N°56 = 1.184,10 m2	1074773	10	02	baldio
PARCELA N°57 = 1.232,20 m2	1074774	10	02	baldio
PARCELA N°58 = 1.159,50 m2	1074775	10	02	baldio
PARCELA N°59 = 1.108,30 m2	1074776	10	02	baldio
PARCELA N°60 = 1.284,20 m2	1074777	10	02	baldio
PARCELA N°61 = 1.365,30 m2	1074778	10	02	baldio
PARCELA N°62 = 1.017,50 m2	1074779	10	02	baldio
PARCELA N°63 = 944,20 m2	1074780	10	02	baldio
Sup. parcial Manz. 210 = 27.942,90 m2				

RESUMEN DE SUPERFICIES

MANZANA 210	Padrón	Recep.	Cuad.	Edif.
PARCELA N°64 = 930,40 m2	1074781	10	02	baldio
PARCELA N°65 = 957,70 m2	1074782	10	02	baldio
PARCELA N°66 = 986,80 m2	1074783	10	02	baldio
PARCELA N°67 = 1.036,90 m2	1074784	10	02	baldio
PARCELA N°68 = 997,50 m2	1074785	10	02	baldio
PARCELA N°69 = 919,90 m2	1074786	10	02	baldio
PARCELA N°70 = 1.381,80 m2	1074787	10	02	baldio
PARCELA N°71 = 1.394,00 m2	1074788	10	02	baldio
PARCELA N°72 = 1.353,20 m2	1074789	10	02	baldio
PARCELA N°73 = 1.258,00 m2	1074790	10	02	baldio
PARCELA N°74 = 1.230,40 m2	1074791	10	02	baldio
PARCELA N°75 = 1.218,30 m2	1074792	10	02	baldio
PARCELA N°76 = 1.212,60 m2	1074793	10	02	baldio
PARCELA N°77 = 1.185,90 m2	1074794	10	02	baldio
PARCELA N°78 = 1.093,50 m2	1074795	10	02	baldio
PARCELA N°79 = 969,20 m2	1074796	10	02	baldio
PARCELA N°80 = 821,60 m2	1074797	10	02	baldio
PARCELA N°81 = 809,90 m2	1074798	10	02	baldio
PARCELA N°82 = 942,10 m2	1074799	10	02	baldio
PARCELA N°83 = 895,90 m2	1074800	10	02	baldio
PARCELA N°84 = 867,70 m2	1074801	10	02	baldio
PARCELA N°85 = 834,30 m2	1074802	10	02	baldio
PARCELA N°86 = 808,50 m2	1074803	10	02	baldio
PARCELA N°87 = 832,30 m2	1074804	10	02	baldio
PARCELA N°88 = 913,60 m2	1074805	10	02	baldio
PARCELA N°89 = 980,80 m2	1074806	10	02	baldio
PARCELA N°90 = 1.068,80 m2	1074807	10	02	baldio
Sup. parcial Manz. 210 = 27.901,60m2				

Sup.Total Manz. 210 = 55.844,50 m2

Nota: La parcela Nº51 esta destinada a servidumbre de Servicios

RESUMEN DE SUPERFICIES

Superficie total Manzana 210	=	55.844,50 m2
Superficie total Mz.Nº210 del Pl.Nº4/33/13	=	55.844,50 m2
Diferencia	=	------------ m2

Los Cerritos S.R.L
Padrón Nº967690- Recep. Concarán
P.A.Nº4/33/13-Parcela Nº26

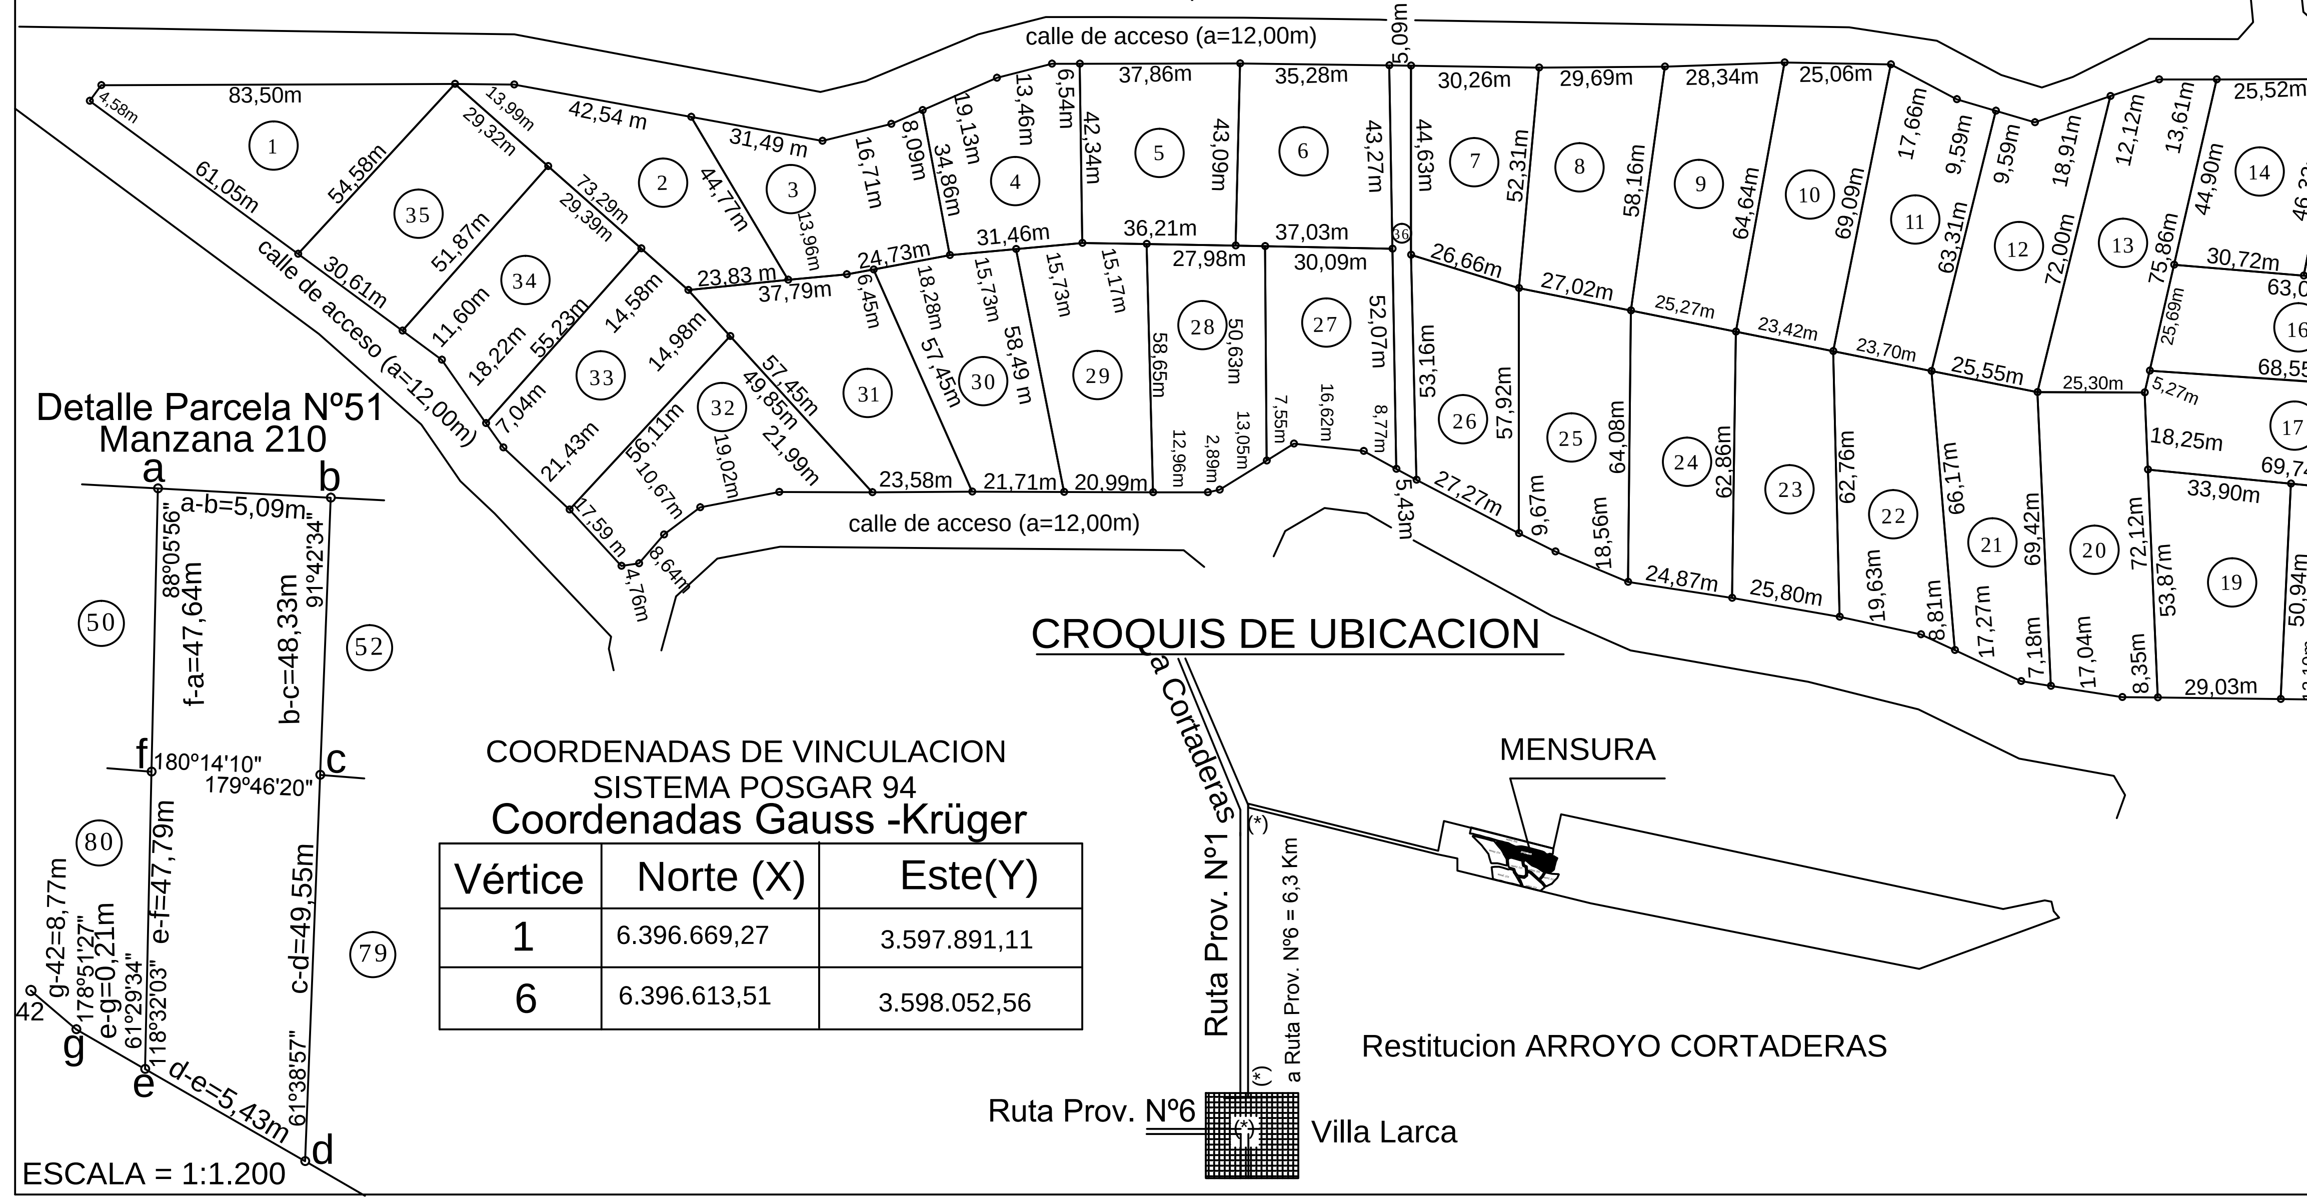

COORDENADAS DE VINCULACION
SISTEMA POSGAR 94

Coordenadas Gauss -Krüger

Vértice	Norte (X)	Este(Y)
1	6.396.669,27	3.597.891,11
6	6.396.613,51	3.598.052,56

ESCALA = 1:1.200

D

CROQUIS DE TÍTULO

PARCELA "A" PLANO 4-105-05
Fracción ubicada sobre Ruta Provincial Nº1 Km.27- Villa Larca

Superficie Total Según Título	= 344 has. 7.266,00 m2
Superficie Total Según desprendimientos	= 10 has. 1.572 ,30 m2
Superficie total Saldo de Titulo	= 334 has. 5.693,70 m2