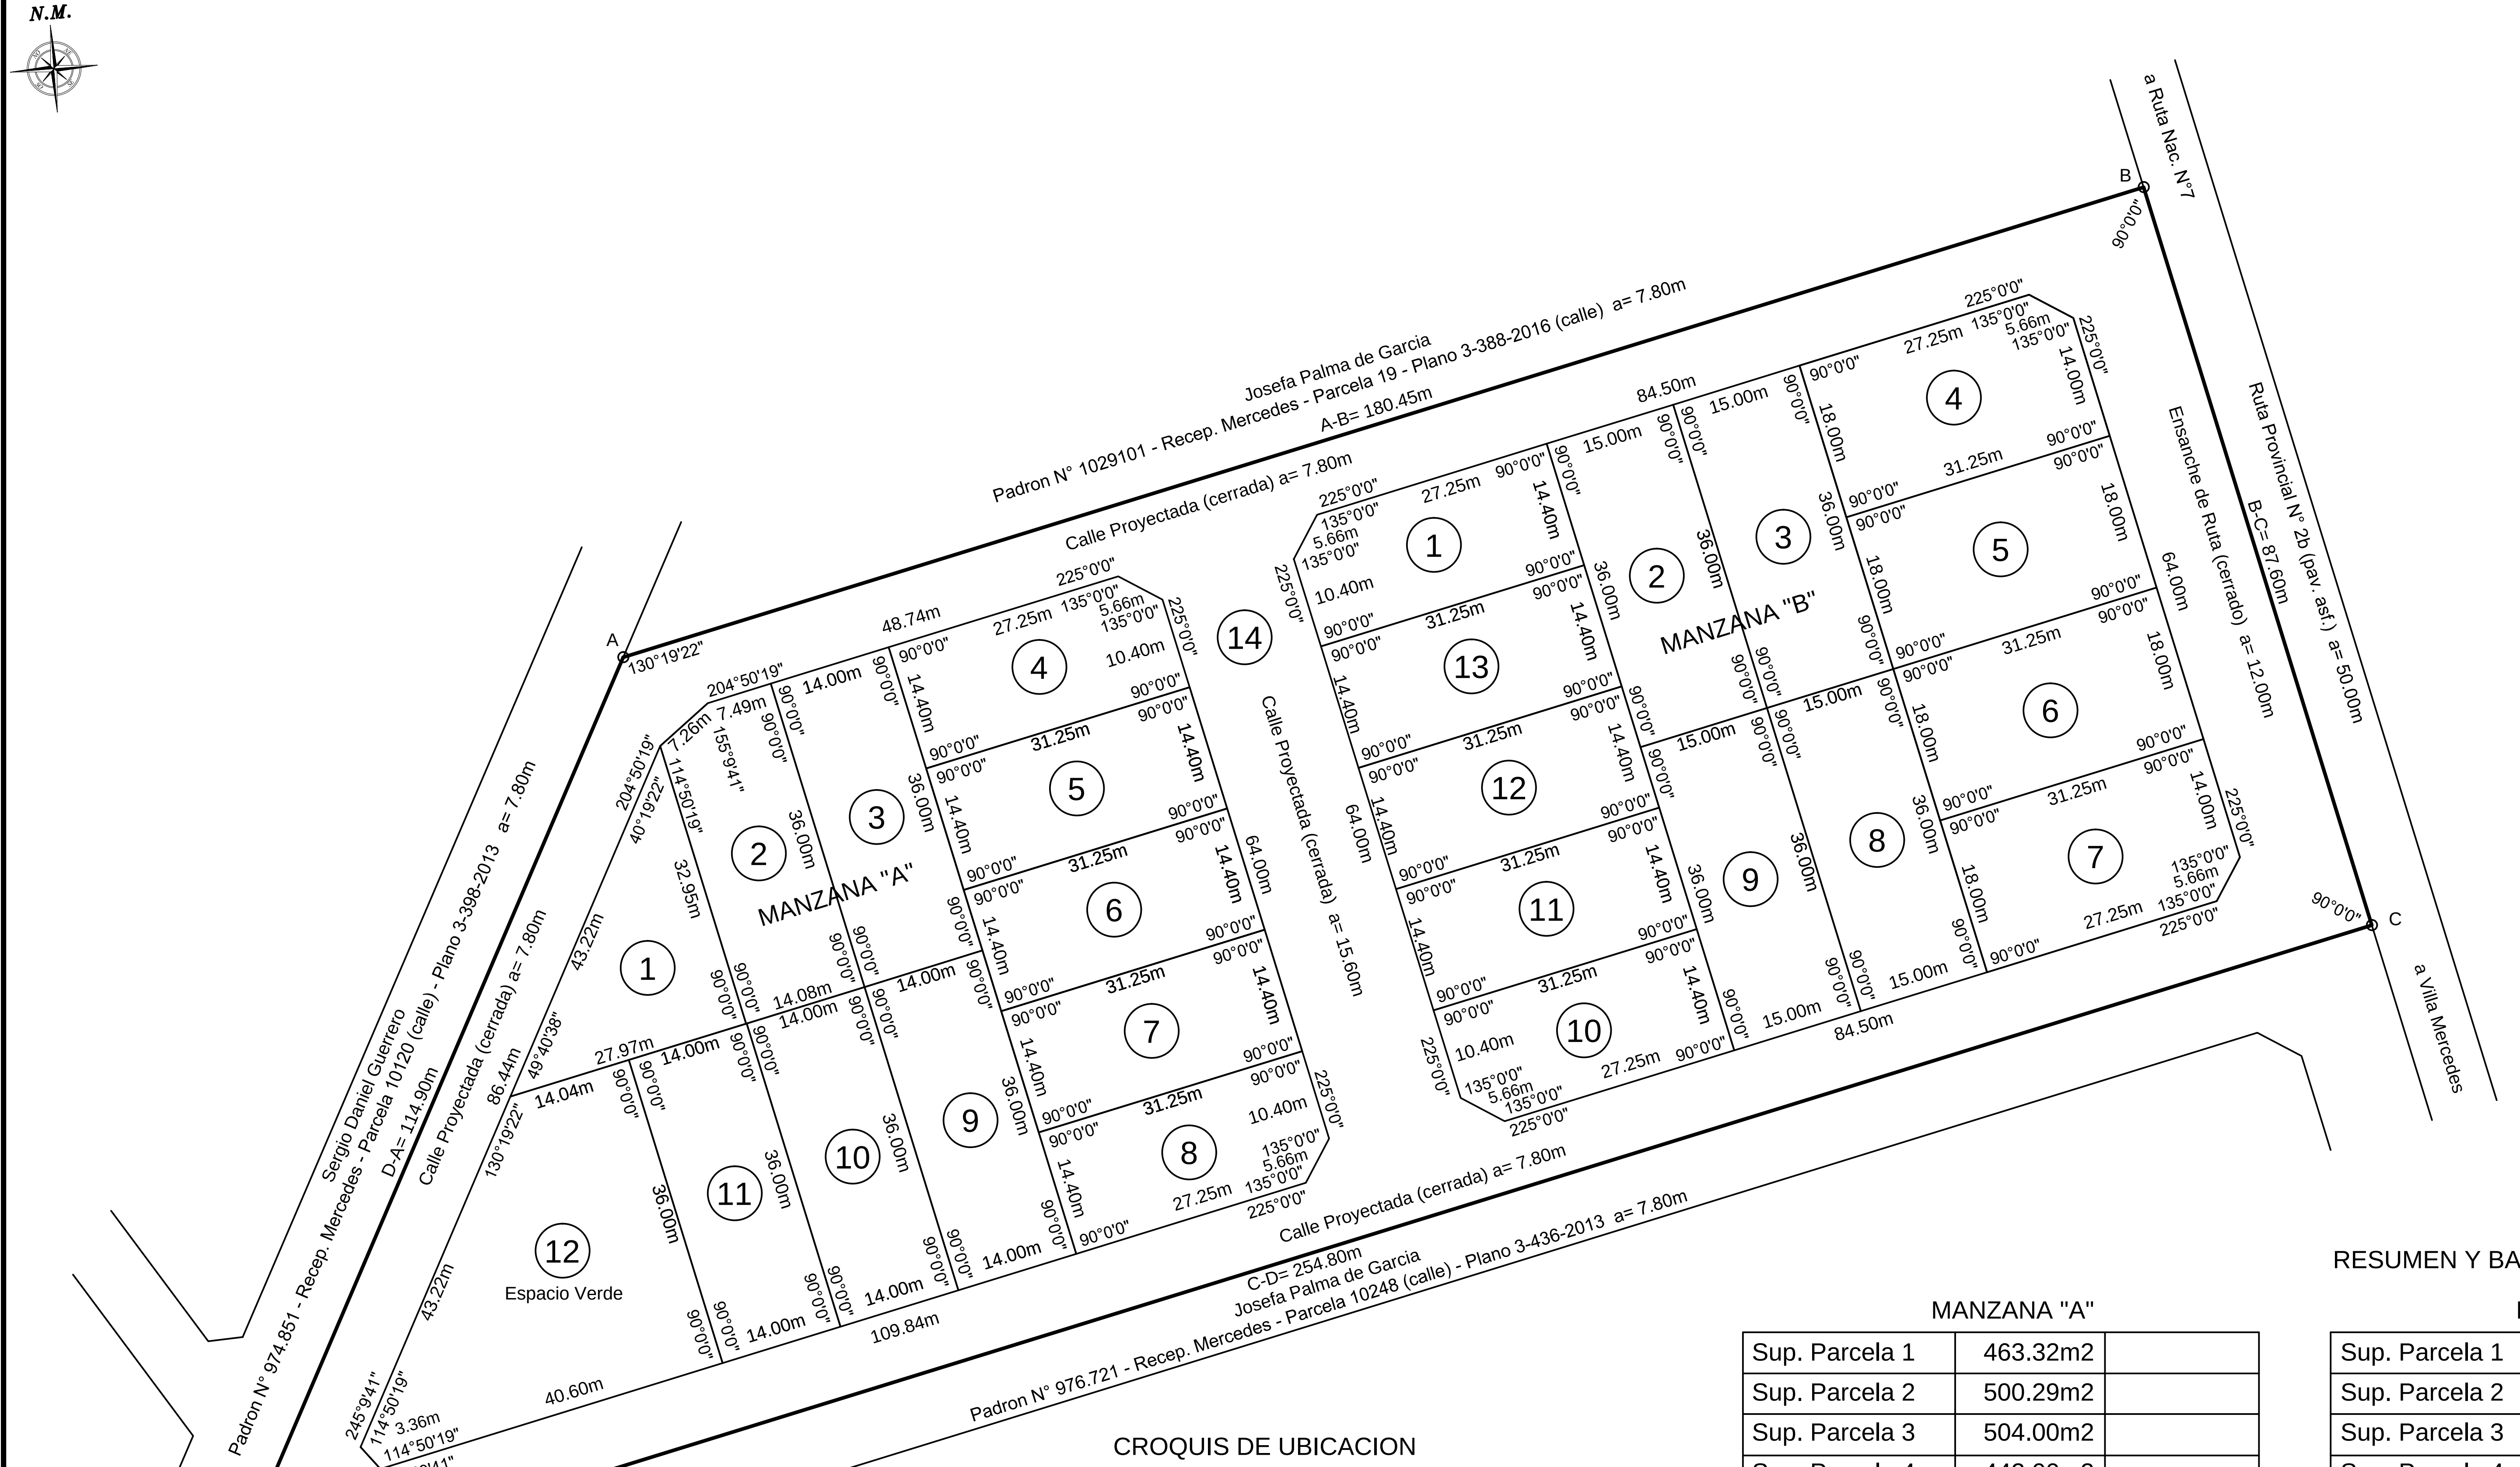
N.M.
Josefa Palma de Garcia
Padron N° 1029101 - Recep. Mercedes - Parcela 19 - Plano 3-388-2016 (calle) a= 7.80m
A-B= 180.45m
Calle Proyectada (cerrada) a= 7.80m
a Ruta Nac. N°7
Ruta Provincial N° 2b (pav. asf.) a= 50.00m
B-C= 87.60m
Ensanche de Ruta (cerrado) a= 12.00m
a Villa Mercedes
Calle Proyectada (cerrada) a= 15.60m
Calle Proyectada (cerrada) a= 7.80m
C-D= 254.80m
Josefa Palma de Garcia
Padron N° 976.721 - Recep. Mercedes - Parcela 10248 (calle) - Plano 3-436-2013 a= 7.80m
Sergio Daniel Guerrero
Padron N° 974.851 - Recep. Mercedes - Parcela 10120 (calle) - Plano 3-398-2013 a= 7.80m
D-A= 114.90m
Calle Proyectada (cerrada) a= 7.80m
A
B
C
130°19'22"
90°0'0"
90°0'0"
MANZANA "A"
MANZANA "B"
Espacio Verde
1
2
3
4
5
6
7
8
9
10
11
12
13
14
48.74m
84.50m
109.84m
40.60m
86.44m
43.22m
32.95m
27.97m
14.04m
14.08m
36.00m
31.25m
27.25m
14.40m
10.40m
5.66m
15.00m
18.00m
64.00m
3.36m
7.49m
7.26m
204°50'19"
40°19'22"
114°50'19"
155°9'41"
49°40'38"
245°9'41"
225°0'0"
135°0'0"

CROQUIS DE UBICACION

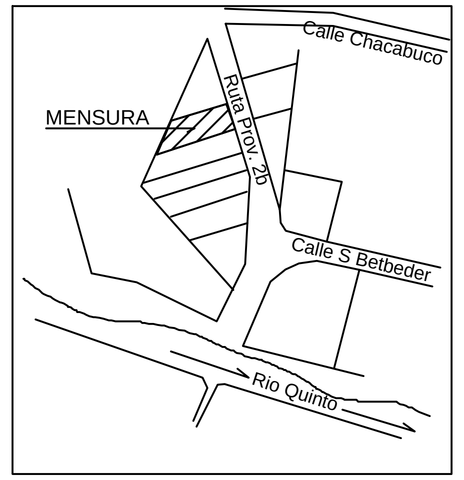

EJIDO MERCEDES

Escala 1 : 300

C

CROQUIS S./TITULO
Parcela 2, plano 3/120/1997
Superficie: 19060.00m2

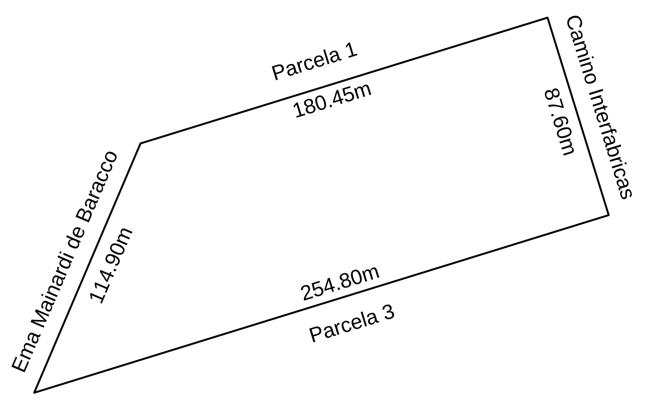

Coordenadas Vinculación

Sistema POSGAR 94 Coordenadas Gauss - Krüger		
Vértice	Este (Y)m	Norte (X)m
A	3546046.18	6274752.03
B	3546218.57	6274805.34

"Las coordenadas han sido determinadas en forma aproximada y al solo efecto del vuelco Cartográfico"

RESUMEN Y BALANCE DE SUPERFICIES

MANZANA "A"

Sup. Parcela 1	463.32m2	
Sup. Parcela 2	500.29m2	
Sup. Parcela 3	504.00m2	
Sup. Parcela 4	442.00m2	
Sup. Parcela 5	450.00m2	
Sup. Parcela 6	450.00m2	
Sup. Parcela 7	450.00m2	
Sup. Parcela 8	442.00m2	
Sup. Parcela 9	504.00m2	
Sup. Parcela 10	504.00m2	
Sup. Parcela 11	504.00m2	
Sup. Parcela 12	1049.48m2	
Total Manzana A	6263.09m2	

Parcela 12 destinada a espacio verde

MANZANA "B"

Sup. Parcela 1	442.00m2	
Sup. Parcela 2	540.00m2	
Sup. Parcela 3	540.00m2	
Sup. Parcela 4	554.50m2	
Sup. Parcela 5	562.50m2	
Sup. Parcela 6	562.50m2	
Sup. Parcela 7	554.50m2	
Sup. Parcela 8	540.00m2	
Sup. Parcela 9	540.00m2	
Sup. Parcela 10	442.00m2	
Sup. Parcela 11	450.00m2	
Sup. Parcela 12	450.00m2	
Sup. Parcela 13	450.00m2	
Sup. Parcela 14	6172.86m2	
Total Manzana B	12800.86m2	

Total Manzana A	6256.99 m2
Total Manzana B	12800.86m2
Total s./Mensura	19063.95 m2
Total s./Titulo	19060.00 m2
Diferencia en mas	3.95 m2

PROVINCIA DE SAN LUIS

3 | 25

Departamento: General Pedernera.-
Partido: Mercedes.-
Lugar: Ruta Prov. N° 2b. Villa Mercedes
Objeto: Division.-
Propietario:

CLAUDIO ALEJANDRO SAENZ (D.N.I.:22.786.391),
MARIO OSCAR FUNES (D.N.I.:12.883.351).-

INSCRIPCION DE DOMINIO	PADRON	RECEPTORIA
Tomo 123 (Ley 3236) de Ped. F° 324 N° 36.349.-	19.318	Mercedes.-

NOMENCLATURA CATASTRAL DE ORIGEN

CIRCUNSCRIPCION	CUADRANTE	SECCION	MANZANA	PARCELA
Ciudad de Mercedes				

OBSERVACIONES:La presente divide la parcela 2 del plano 3/120/97 aprob. en 19 de Febrero de 1998, confeccionado por el Agrim. Jorge del Bosco.
Los vertices estan materializados estacas de madera.
Expediente Municipal 2025-3183 E MUN

Villa Mercedes (San Luis).- 13 de Junio de 2025.-

JUAN JOSE BLANCO LAXAGUE
AGRIMENSOR
MAT. 296 C.A.S.L.